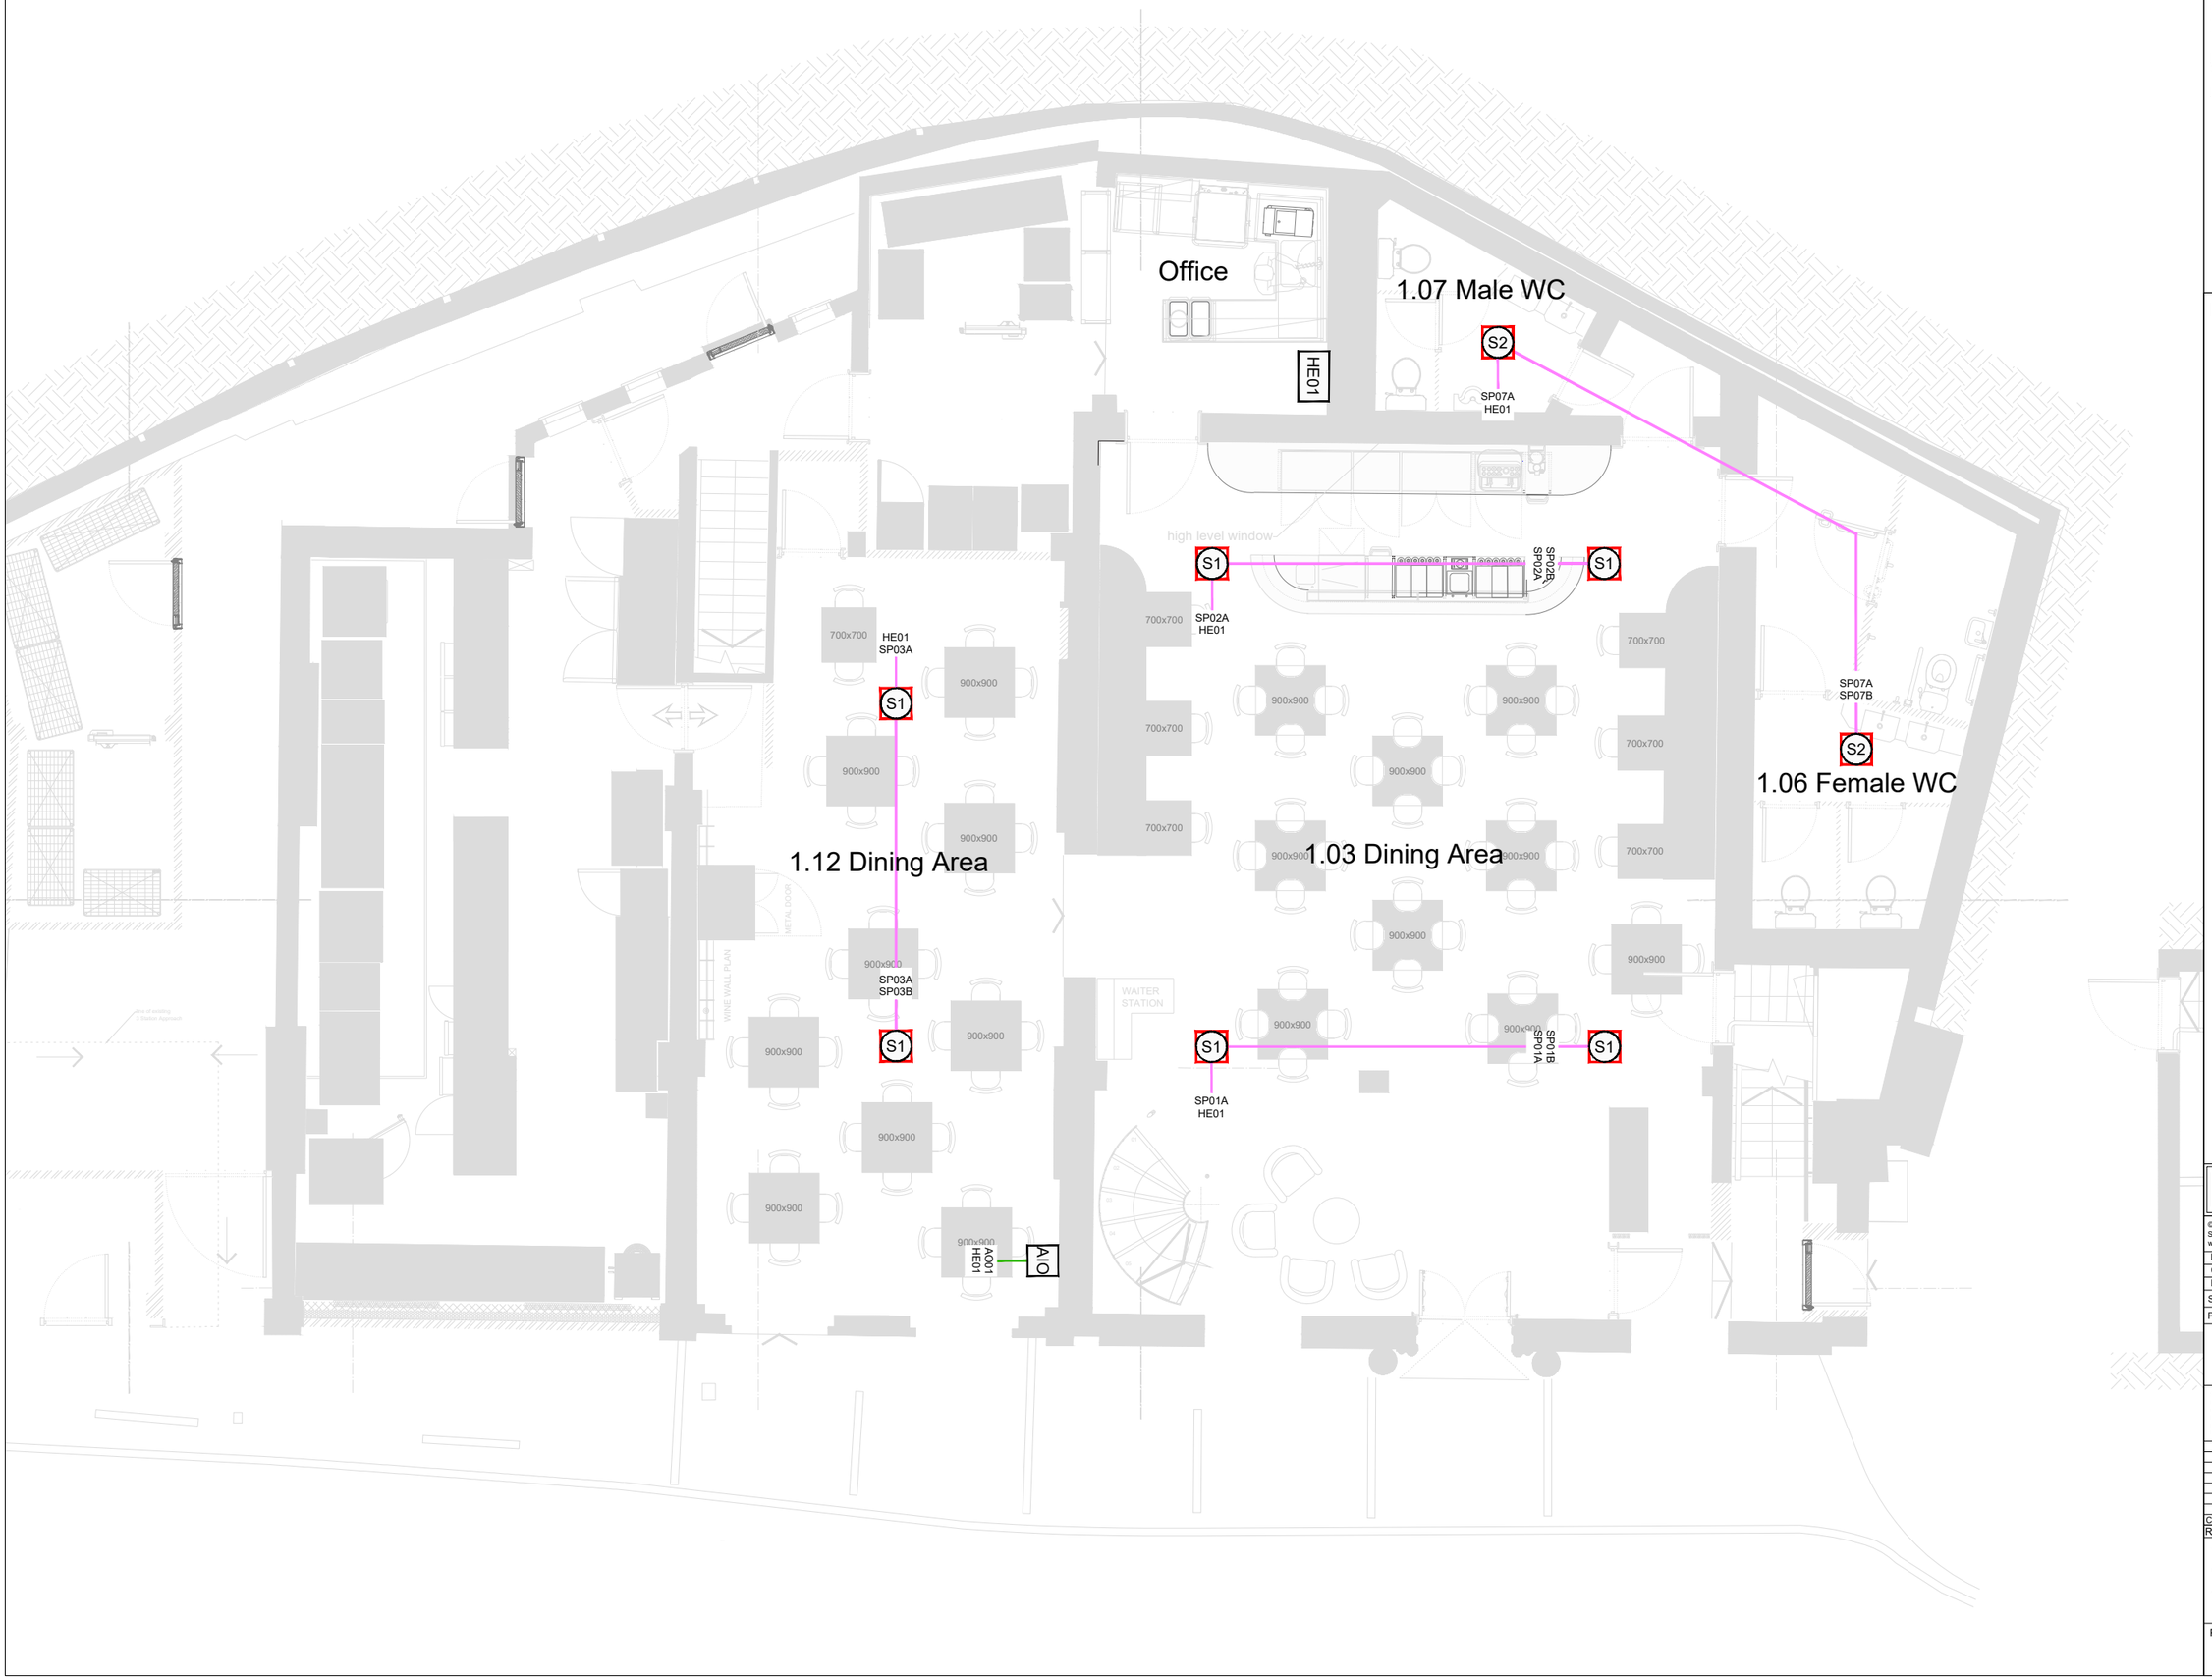

NOTES

To Be Read In Conjuction With Schematic Ref:
TBR-SMA-XX-00-DR-SC-AV-10001
TBR-SMA-XX-01-DR-SC-AV-10001
TBR-SMA-XX-ZZ-DR-SC-AV-10001

Reference Drawings:
35-03_GF Elecrical.pdf

For setting out please see:

LEGEND

Item Example

M1 — "M1" Wall Mounted Media Plate 01
"Cables" 2x CAT6A 1x WF100
M102 — "M1" Item ID "02" Unique Number
HE01 — "HE01" Head End

Head End Equipment

HExx — AV Rack
8no. Speaker Cables to Speaker Locations

By Others
- LV (230V) Power
- 2no. CAT6 Cables to TV Locations
- Landlords Network Connection(s)

Wall Plates

DP — CAT6 Point for TV Audiofeed to amplifier (By Others)
AIO — DANTE Audio Input/Output Plate (4no. XLR3)
AV — Video Input Plate (1no. HDMI & 3.5mm Audio)

Speaker Types

S1 — Sonance VX-86R Ceiling Speaker
S2 — Sonance VP-86R SST/SUR Ceiling Speaker

Cable Types

Speaker Cable
TBC
CAT6a Cable F/FTP
Nexans [N100.692G-OC]

Misc. Equipment

Hoody Hoody2 Fire Hood

FOR CONSTRUCTION

© Copyright. All rights to this drawing and its design are the property of SmartComm Ltd. Any use or duplication of this drawing is strictly prohibited without prior written permission of SmartComm Ltd.

Drawn By	CL	12/04/2024	
Checked By	RB	12/04/2024	
Issued By	RB	12/04/2024	
SCALE	NOT TO SCALE		
PAGE SIZE	A1		

smartcomm
integrating technology with vision

Smartcomm Ltd
Halifax Road
Cressex Business Park
High Wycombe
Buckinghamshire
HP12 3SN

Tel: +44 (0)1494 471 912
E-mail: info@smartcomm.co.uk
Web: www.smartcomm.co.uk

Rev	Description	Date	Name
			CL
C01	FOR CONSTRUCTION	18/07/2024	CL

THE BANK RESTAURANT
GROUND FLOOR
AV LAYOUT

Project	Orig.	Vol.	Level	Type	Role	Number	Rev.
TBR	SMA	XX	00	DR	AV	10001	C01