
## TV AUDIO INTEGRATION

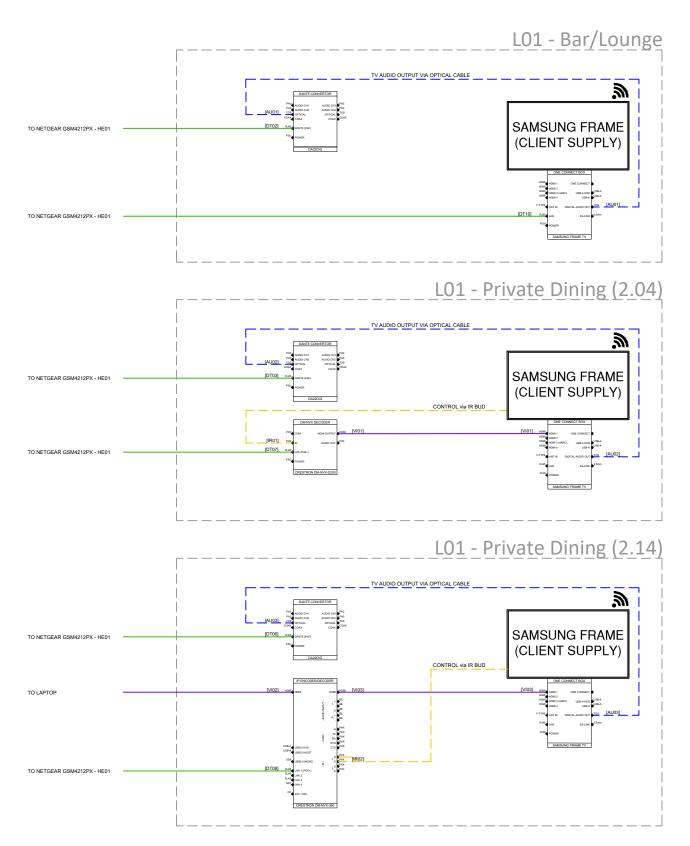

## NOTES

To Be Read In Conjuction With Schematic Ref: TBR-SMA-XX-01-DR-SC-10001

Reference Drawings:

For setting out please see:

## LEGEND

- 2 CORE SPEAKER CABLE

- NOX - CAT 6 GREEN - DATA - NVX
- GLAN- CAT 6 GREEN - DATA - QLAN
- VORP - CAT 6 GREEN - DATA - VOIP

STARQUAD

HDMI CABLE

WF100 RF/SAT COA

----- 8G CABLE

6 CORE CONTROL
FIBRE
3 CORE AND EARTH

REVISION CLOUD

50 Ω LOW LOSS COAX CABLE

75 Ω COAX CABLE

DMX CABLE

DVI

—— DISPLAYPORT

—— USB 2.0

—— USB 3.0

## FOR CONSTRUCTION

© Copyright. All rights to this drawing and its design are the property of SmartComm Ltd. Any use or duplication of this drawing is strictly prohibite without prior written permission of SmartComm Ltd.

Drawn By CL 12(04/2024

Chacked By DB 13(04/2024)

Issued By RB 1:

SCALE NOT TO SCALE

PAGE SIZE A1

smartcomm integrating technology with vision • • •

C01 FOR CONSTRUCTION 18/0 Per Description D
THE BANK RESTAURANT TV AUDIO INTEGRATION

AV SCHEMATIC

oject Orig. Vol. Level Type Role Number Rev.

BR SMA XX 01 DR SC 10001 C01